


# STOP LIGHT

FROM POWER SOURCE SYSTEM (SEE PAGE 46)

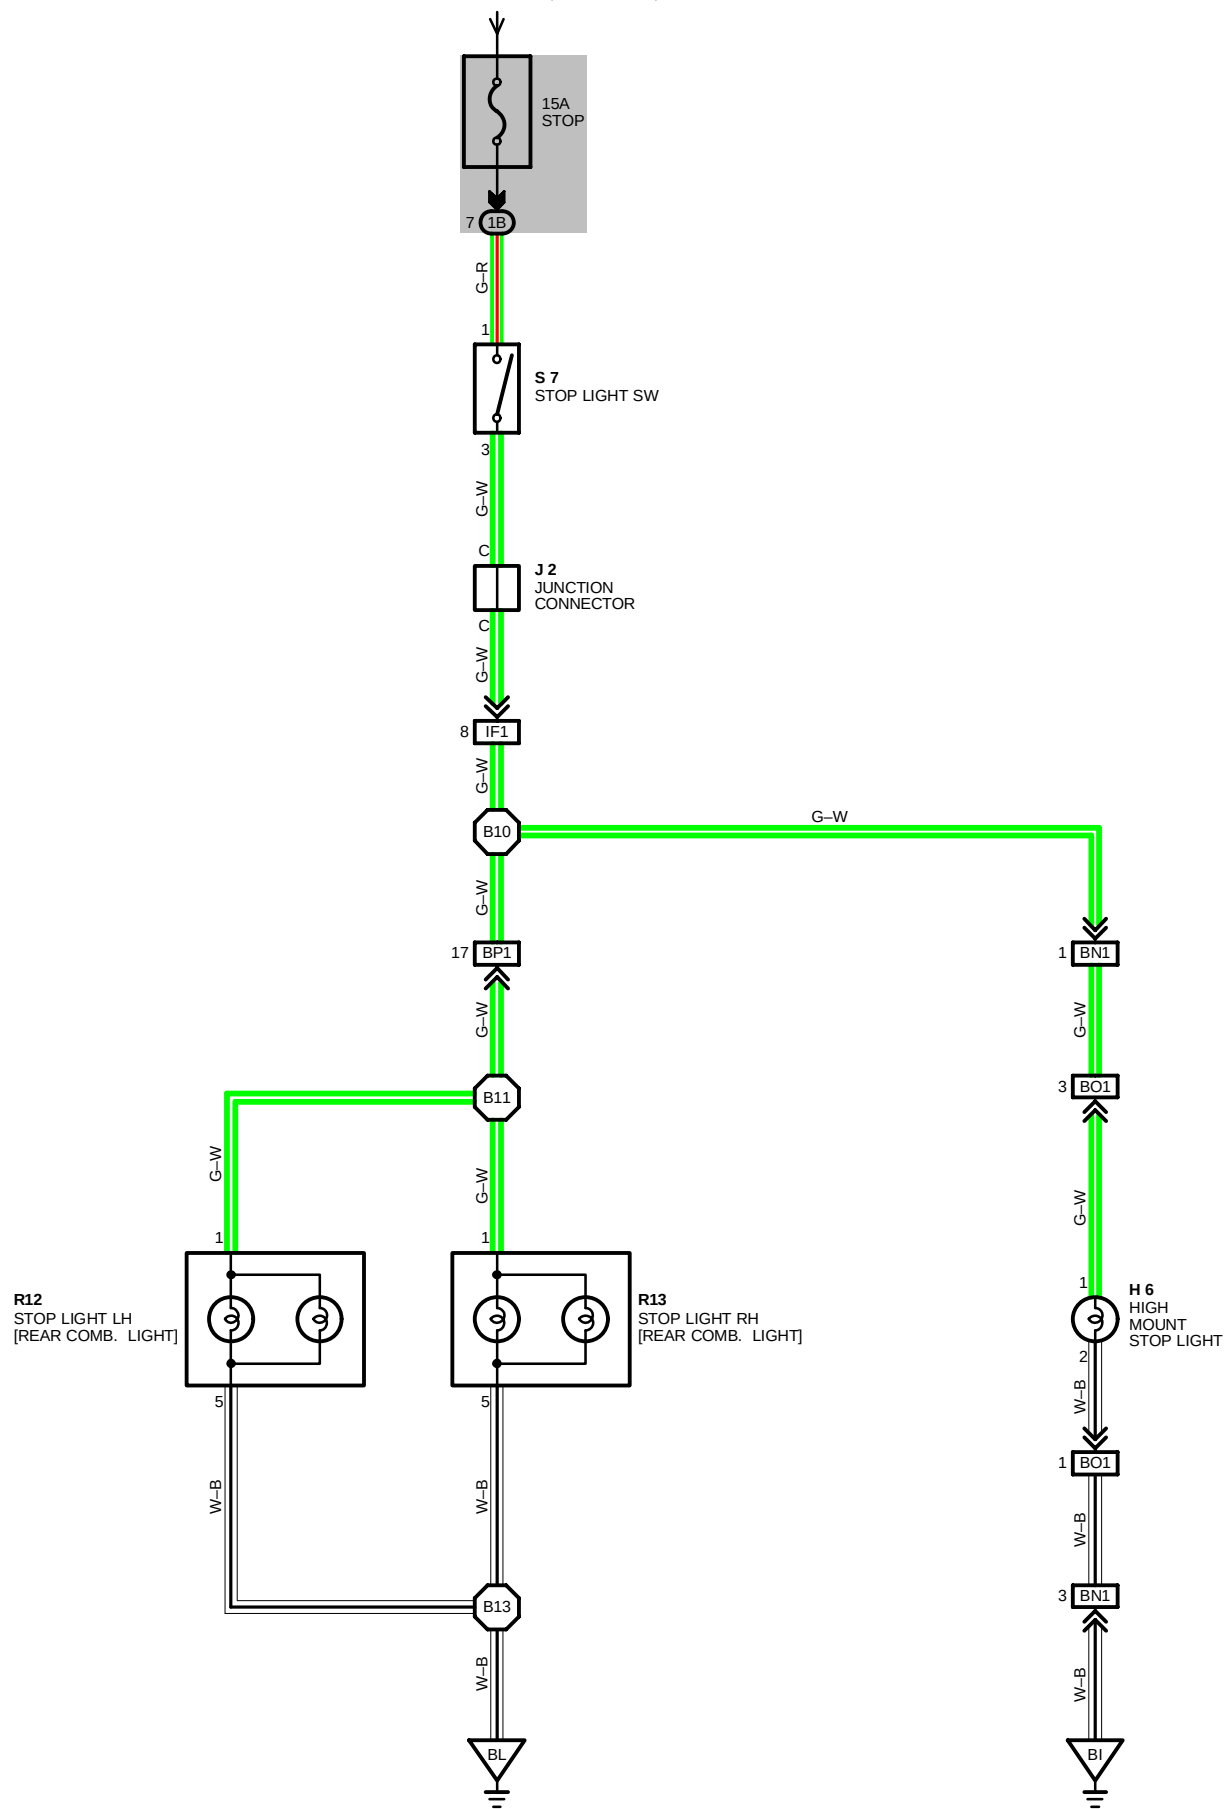

## SERVICE HINTS

### S 7 STOP LIGHT SW

1-3: CLOSED WITH BRAKE PEDAL DEPRESSED

### : PARTS LOCATION

| CODE | SEE PAGE | CODE | SEE PAGE | CODE | SEE PAGE |
|------|----------|------|----------|------|----------|
| H 6  | 27       | R12  | 27       | S 7  | 26       |
| J 2  | 26       | R13  | 27       |      |          |

### : JUNCTION BLOCK AND WIRE HARNESS CONNECTOR

| CODE | SEE PAGE | JUNCTION BLOCK AND WIRE HARNESS (CONNECTOR LOCATION) |
|------|----------|------------------------------------------------------|
| 1B   | 18       | COWL WIRE AND J/B NO. 1 (LEFT KICK PANEL)            |

### : CONNECTOR JOINING WIRE HARNESS AND WIRE HARNESS

| CODE | SEE PAGE | JOINING WIRE HARNESS AND WIRE HARNESS (CONNECTOR LOCATION)               |
|------|----------|--------------------------------------------------------------------------|
| IF1  | 30       | FLOOR WIRE AND COWL WIRE (LEFT KICK PANEL)                               |
| BN1  | 34       | BACK DOOR NO. 1 WIRE AND FLOOR WIRE (LEFT SIDE OF PACKAGE TRAY TRIM)     |
| BO1  | 34       | BACK DOOR NO. 1 WIRE AND BACK DOOR NO. 1 SUB WIRE (BACK DOOR UPPER LEFT) |
| BP1  | 34       | FLOOR WIRE AND LUGGAGE ROOM WIRE (LEFT QUARTER PANEL CENTER)             |

### : GROUND POINTS

| CODE | SEE PAGE | GROUND POINTS LOCATION       |
|------|----------|------------------------------|
| BI   | 34       | UNDER THE LEFT CENTER PILLAR |
| BL   | 34       | BACK PANEL CENTER            |


### : SPLICE POINTS

| CODE | SEE PAGE | WIRE HARNESS WITH SPLICE POINTS | CODE | SEE PAGE | WIRE HARNESS WITH SPLICE POINTS |
|------|----------|---------------------------------|------|----------|---------------------------------|
| B10  | 34       | FLOOR WIRE                      | B13  | 34       | LUGGAGE ROOM WIRE               |
| B11  | 34       | LUGGAGE ROOM WIRE               |      |          |                                 |

H 6




J 2

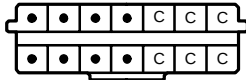

(HINT : SEE PAGE 7)

R12, R13

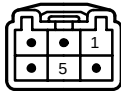

S 7

